

不动产测绘报告书

项目名称： 道县皮革厂家属楼3栋私人建房

委托方： 道县皮革厂家属楼3栋全体业主

测绘单位： 湖南湘达土地规划设计咨询有限公司

房产面积计算说明

一、测量依据

- 1、国家标准《房产测量规范》GB/T17986-2000。
- 2、《湖南省建筑工程竣工综合测量和建筑面积测算规则》。
- 3、委托人提供的有关资料。

二、本报告中使用的长度单位为米，面积单位为平方米。房屋分层分户平面图上所示尺寸为点中(轴线)尺寸，墙体厚度按0.2m计算，阳台外边线为实线的阳台为封闭阳台，阳台外边线为虚线的阳台为不封闭阳台。

三、面积计算

- 1、本报告是根据委托方的要求，采用手持式红外线测距仪或钢卷尺对房屋进行实地丈量，根据实际尺寸绘制分层分户平面图。
- 2、建筑面积是采用建设部认证的《项目测绘》软件计算及分摊。

四、其它

- 1、本报告所述面积，是指按现场勘测该房产的实际建筑面积、房屋登记面积以不动产登记部门确认的面积为准。
- 2、本报告绘制的房产分层分户图不反映房屋内部结构。
- 3、本报告为实测成果，不能作为不动产权属证明。
- 4、本报告是委托方申请不动产登记的必要件，在办理不动产登记时，与其它有关资料一并交不动产登记部门。
- 5、我方与委托方没有利害关系或偏见，也与有关当事人没有利害关系或偏见。
- 6、本报告中陈述的事实是真实和准确的，保证本报告中所涉及的测量成果和计算成果是客观、公正、准确和规范的。我方对报告中涉及的房产测绘成果质量负责。
- 7、本成果报告在正式提交前，已提请委托方检查校对。
- 8、委托方对房产测绘成果有异议的，按《房产测绘管理办法》的规定，可以委托国家认定的房产测绘成果鉴定机构鉴定。
- 9、本报告一式两份，一份交委托方，一份由测绘单位存档备案。

房产勘测成果表

测绘类型：实测

申请人	道县皮革厂家属楼3栋全体业主					
坐落描述	道县月岩西路					
不动产单元号						
房屋状况	房屋结构	砖混结构	建筑时间		用途	住宅
	房屋总层数	5	其中	地下		
				地面	5	
				附层		
	四至墙界		东	自墙	南	自墙
西			自墙	北	自墙	
测绘范围	整栋					
已变更需注销的不动产单元号	无					
勘测结论	该房为自建房，建筑面积2205.05m²，整栋为住宅(实际用途)。 测绘员：杨敬微					
审核意见	测绘成果质量合格，拟同意出具测绘报告。 审核人：周梅利 日期：2026.4.14					

一、本报告无测绘单位公章、无骑缝章无效。

不动产单元号:

房屋结构: 砖混结构

房屋坐落: 道县月岩西路

测绘类型: 实测

建筑面积: 2205.05m²

户室面积对照表

层次	户号	户室号	建筑面积	套内面积	阳台面积	分摊面积	户室结构	用途
1	0001	101	74.65	68.77	2.65	5.88	砖混结构	住宅
		102	73.415	67.535	2.65	5.88	砖混结构	住宅
		103	73.415	67.535	2.65	5.88	砖混结构	住宅
		104	73.415	67.535	2.65	5.88	砖混结构	住宅
		105	73.415	67.535	2.65	5.88	砖混结构	住宅
		106	72.70	66.82	2.55	5.88	砖混结构	住宅
2	0001	201	74.65	68.77	2.65	5.88	砖混结构	住宅
		202	73.415	67.535	2.65	5.88	砖混结构	住宅
		203	73.415	67.535	2.65	5.88	砖混结构	住宅
		204	73.415	67.535	2.65	5.88	砖混结构	住宅
		205	73.415	67.535	2.65	5.88	砖混结构	住宅
		206	72.70	66.82	2.55	5.88	砖混结构	住宅
3	0001	301	74.65	68.77	2.65	5.88	砖混结构	住宅
		302	73.415	67.535	2.65	5.88	砖混结构	住宅
		303	73.415	67.535	2.65	5.88	砖混结构	住宅
		304	73.415	67.535	2.65	5.88	砖混结构	住宅
		305	73.415	67.535	2.65	5.88	砖混结构	住宅
		306	72.70	66.82	2.55	5.88	砖混结构	住宅
4	0001	401	74.65	68.77	2.65	5.88	砖混结构	住宅
		402	73.415	67.535	2.65	5.88	砖混结构	住宅
		403	73.415	67.535	2.65	5.88	砖混结构	住宅
		404	73.415	67.535	2.65	5.88	砖混结构	住宅
		405	73.415	67.535	2.65	5.88	砖混结构	住宅
		406	72.70	66.82	2.55	5.88	砖混结构	住宅
5	0001	501	74.65	68.77	2.65	5.88	砖混结构	住宅
		502	73.415	67.535	2.65	5.88	砖混结构	住宅
		503	73.415	67.535	2.65	5.88	砖混结构	住宅
		504	73.415	67.535	2.65	5.88	砖混结构	住宅
		505	73.415	67.535	2.65	5.88	砖混结构	住宅
		506	72.70	66.82	2.55	5.88	砖混结构	住宅
合计			2205.05	2028.65	79.00	176.40		



不动产单元号:

房屋结构: 砖混结构

房屋坐落: 道县月岩西路

楼层面积对照表

建筑面积: 2205.05m²

层次	层建筑面积	层套内面积	层阳台面积	层公用面积	层半墙面积	层高
1	441.01	378.43	15.80	35.88	26.70	≥2.2
2	441.01	378.43	15.80	35.88	26.70	≥2.2
3	441.01	378.43	15.80	35.88	26.70	≥2.2
4	441.01	378.43	15.80	35.88	26.70	≥2.2
5	441.01	378.43	15.80	35.88	26.70	≥2.2
合计	2205.05	1892.15	79.00	179.40	133.50	

土地分摊表

不动产单元号:

房屋结构: 砖混结构


房屋坐落: 道县月岩西路

土地面积: 456.60(m²)

层次	户室01	户室02	户室03	户室04	户室05	户室06	小计
1	15.46	15.20	15.20	15.20	15.20	15.06	91.32
2	15.46	15.20	15.20	15.20	15.20	15.06	91.32
3	15.46	15.20	15.20	15.20	15.20	15.06	91.32
4	15.46	15.20	15.20	15.20	15.20	15.06	91.32
5	15.46	15.20	15.20	15.20	15.20	15.06	91.32
合计							456.60

房屋分层平面图

宗地代码		结构	砖混结构	专有建筑面积	1892.15
幢号	F001	总层数	5	分摊建筑面积	312.90
所在层次	第1-5层			建筑面积	2205.05
坐落	道县月岩西路				

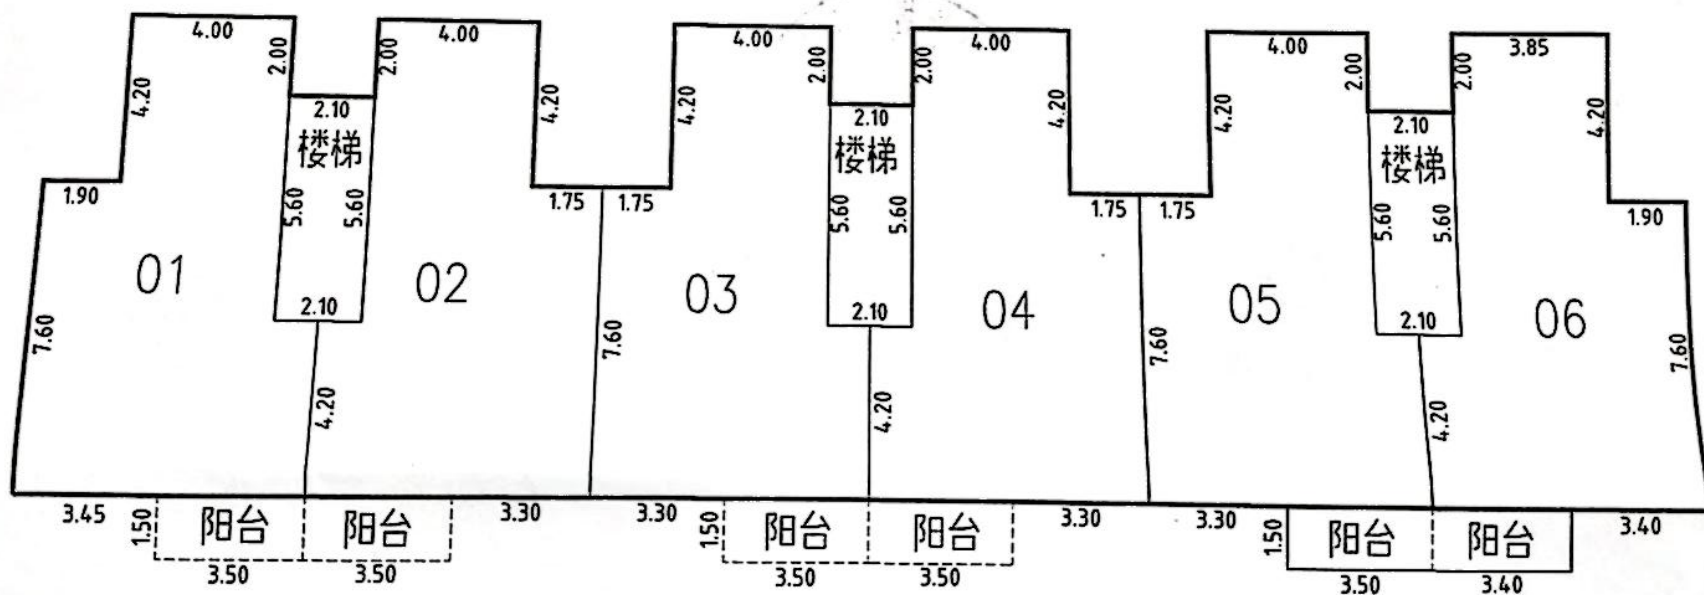

1:100

绘图时间: 2026年4月27日